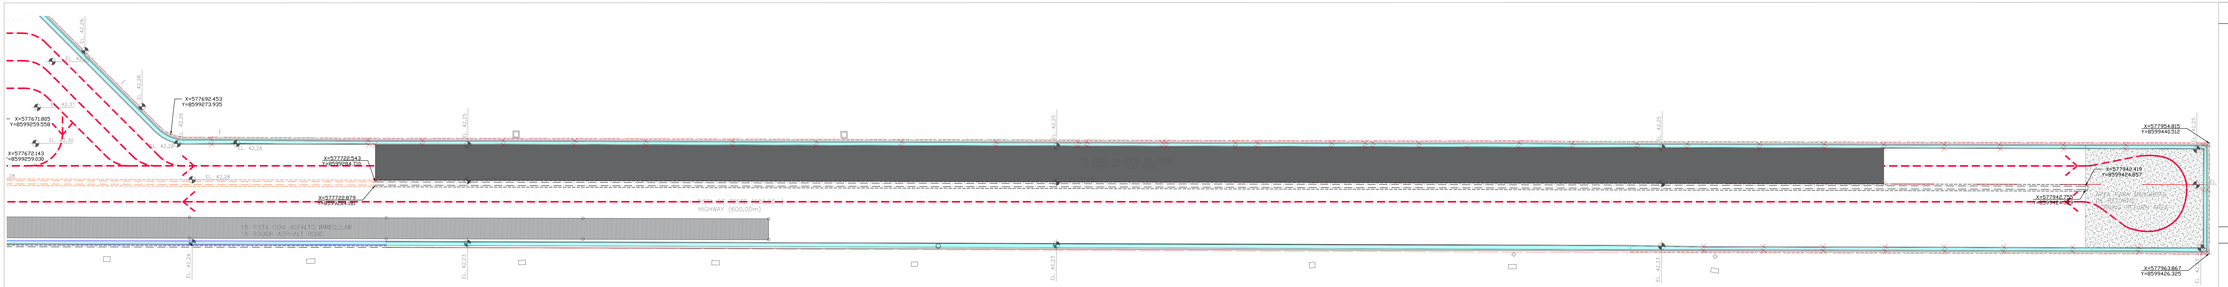

PLANTA BAIXA - LOCAÇÃO DAS DEFENSAS METÁLICAS - PARTE 1

ESCALA 1/250

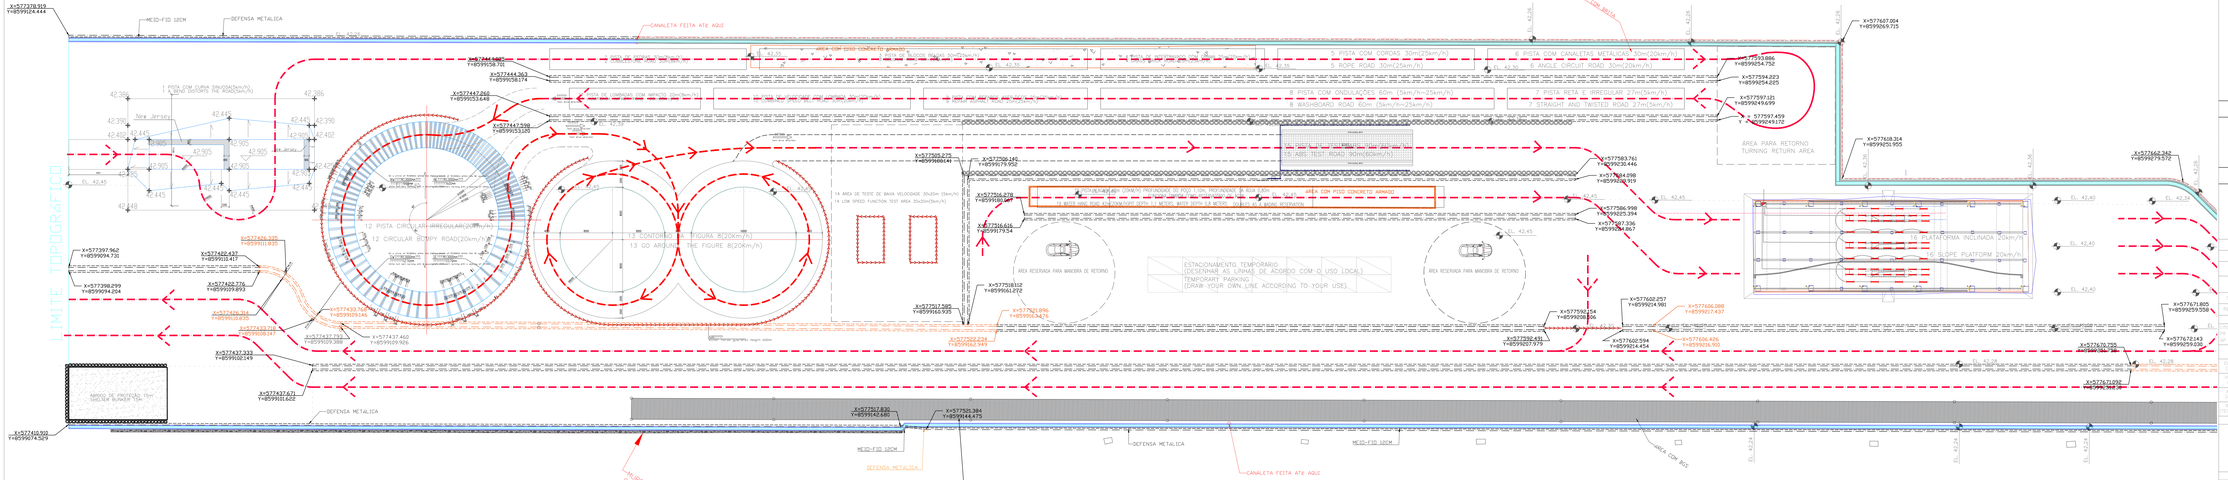

PLANTA BAIXA - LOCAÇÃO DAS DEFENSAS METÁLICAS - PARTE 2

ESCALA 1/250

NOTAS (NOTES)

LEGENDA (LEGEND)

DEFENSA METÁLICA

(TODAS AS COORDENADAS DAS DEFENSAS METÁLICAS SÃO REFERENTES AO EIXO DOS POSTES DE FIXAÇÃO DAS LÂMINAS)

DOCUMENTOS DE REFERÊNCIA (REFERENCE DOCUMENTS)

PLANTA CHAVE (KEY PLANT)

REV.	DATE DATA	DESCRIÇÃO DESCRIPTION	EMISSÃO DESIGNED	VERIFICAÇÃO VERIFICATION	APROVAÇÃO APPROVAL
0	22/01/2024	EMISSÃO INICIAL / ISSUE NO	EA	RC	

REVISÕES (REVIEWS)

TIPOS DE EMISSÃO (ISSUE CODES): P - PRELIMINAR (PR - PRELIMINARY); A - APROVAÇÃO (AP - APPROVAL); C - CONSTRUÇÃO (IC - CONSTRUCTION); U - USO LOCAL (LU - LOCAL USE); R - REVISÃO (RS - REVISED); CONSTRUCTION

ELABORADOR DESIGNER	BRUNO ALMEIDA	22/01/2024	KT00334-3	
CONFERIDOR CHECKER	RAMON CRUZ	22/01/2024	TP00511R-3	
APROVADOR APPROVER				
GERENTE DO PROJETO PROJECT MANAGER	PAULO VITOR	22/01/2024	T10284	

CLIENTE (CLIENT)

BYD Auto Industry (Brasil) Ltda.

SEPENG ENGENHARIA

ENGENHARIA SHD LTDA (SHD ENGINEERING)

GERENTE DO PROJETO (PROJECT MANAGER): PAULO VITOR

BYD Auto Industry (Brasil) Ltda.

AÇÃO (WHY) FOR: CANCAR - BAHIA | CANCAR - BAHIA - BRASIL

DOCUMENTO (DOCUMENT): DW-AMD-J-0000-000

CÓDIGO (CODE): CYTO

PÁTIO DE TESTES / TEST TRACK

LOCAÇÃO DAS DEFENSAS METÁLICAS / LOCATION OF METAL DEFENSES

ESCALAS (SCALES): 1/250

NÚMERO (NUMBER): DW-PH20.00.GE/ED.PPO-121

REVISÃO (REVISION): 0

FOLHA (SHEET): E1