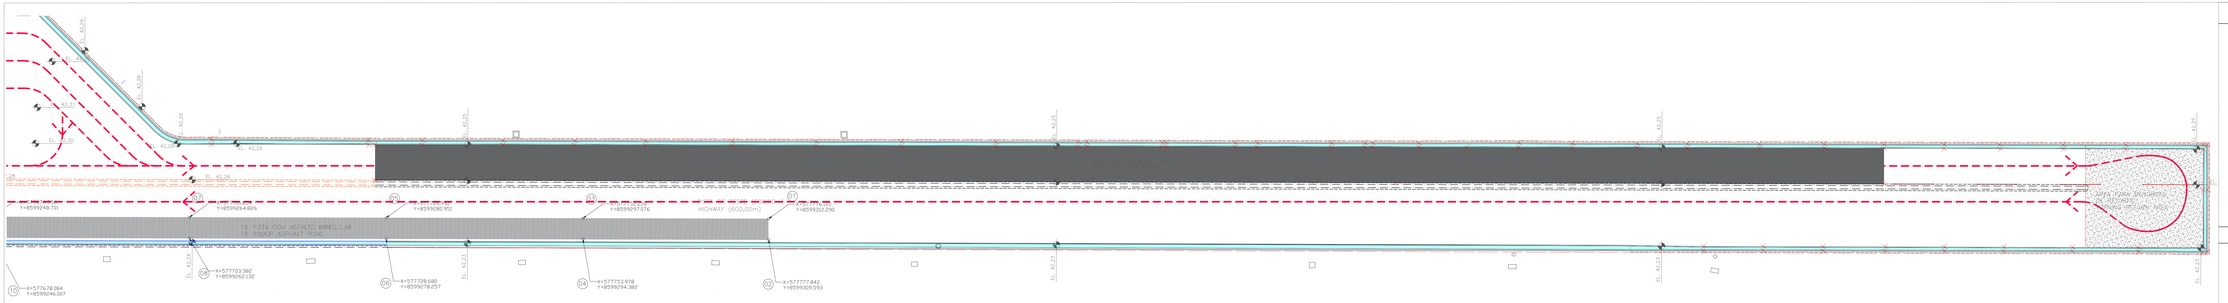

PLANTA BAIXA - LOCAÇÃO DAS PISTAS FASE 03 - PARTE 1

ESCALA 1/250

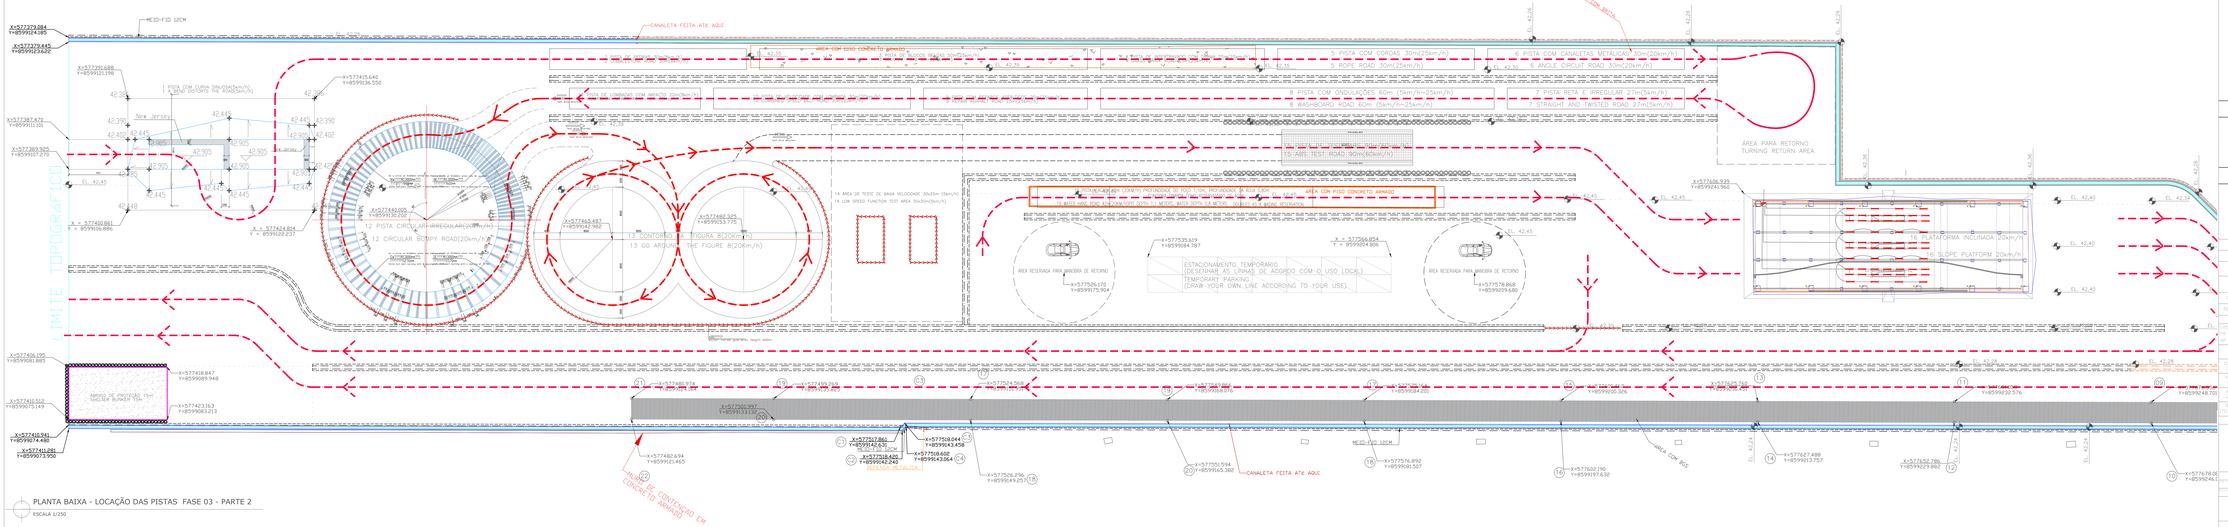

PLANTA BAIXA - LOCAÇÃO DAS PISTAS FASE 03 - PARTE 2

ESCALA 1/250

NOTAS (NOTES)

LEGENDA (LEGEND)

DOCUMENTOS DE REFERÊNCIA (REFERENCE DOCUMENTS)

PLANTA CHAVE (KEY PLANT)

REV	DATA DATE	DESCRIÇÃO DESCRIPTION	TÉCNICO DESIGNER	VERIFICAÇÃO VERIFICATION	APROVAÇÃO APPROVAL
0	14/01/2024	EMISSÃO INICIAL / 初次发布	RA	RC	

REVISÕES (REVISIONS)

PROPÓSITOS DE EMISSÃO (ISSUE CODES): PR - PRELIMINAR (PR - PRELIMINARY) AP - APROVAÇÃO (AP - APPROVAL) CO - CONSTRUÇÃO (CO - CONSTRUCTION) LO - LEGAL (LO - LEGAL)

	CLASSIFICADOR DESIGNATOR	DATA DATE	CPEA / CREA
CLASSIFICADOR DESIGNATOR	BRUNNO ALMEIDA	14/01/2024	171583W-3
CONFERIDOR CHECKER	RAMON CRUZ	14/01/2024	191551W-3
APROVADOR APPROVER			
GERENTE DE MANAGER	PAULO VITOR	14/01/2024	111228A

SEPENG ENGENHARIA
AVENIDA ANHAIA, 1010 - SÃO PAULO - SP

BYD BRAZIL PROPERTIES
Avenida Hary Fiat, 3000 - Polo Industrial de Camaçari

REVISÃO VIGENTE / CURRENT REVISION	CIMACAR - BAHIA	CIMACAR - BAHIA	BRASIL
DW-AMD-H2000-001			

CLIENTE / CLIENT: CYTO

PÁTIO DE TESTES / TEST TRACK
LOCAÇÃO DAS PISTAS / TRACK PLACEMENT

ESCALAS / SCALES: 1/250
NÚMERO / NUMBER: DW-PH20.00.GE/ED.PP0-120
REVISÃO / REVISION: 0
FOLHA / SHEET: E1