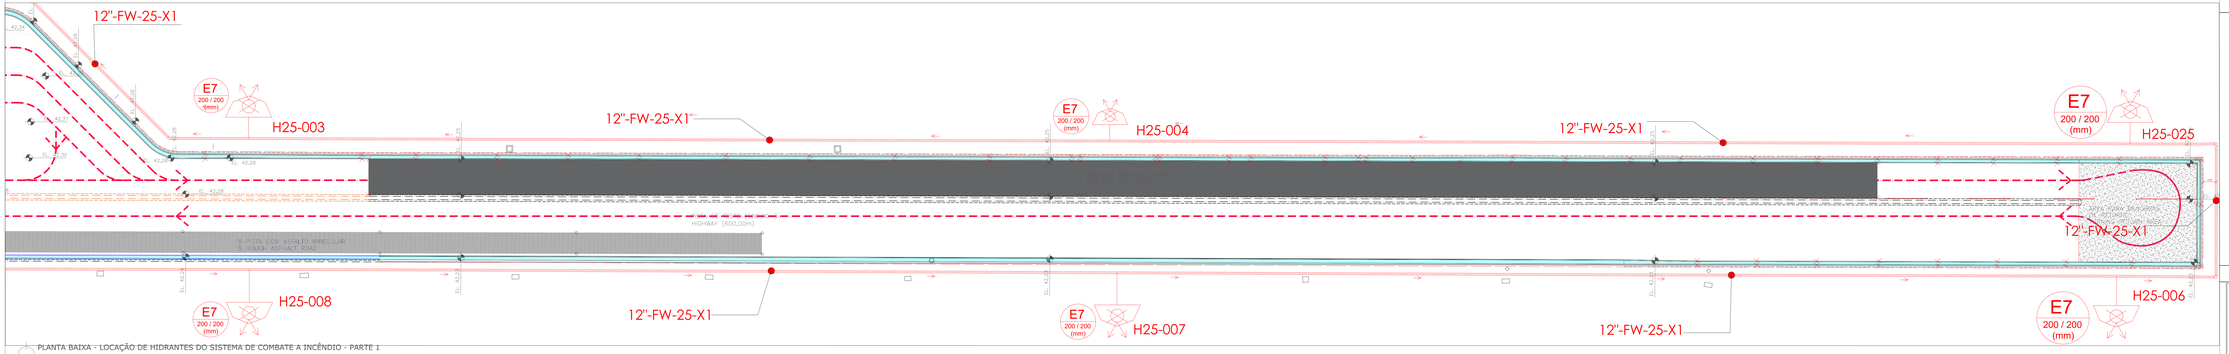

PLANTA BAIXA - LOCAÇÃO DE HIDRANTES DO SISTEMA DE COMBATE A INCÊNDIO - PARTE 1

ESCALA 1/250

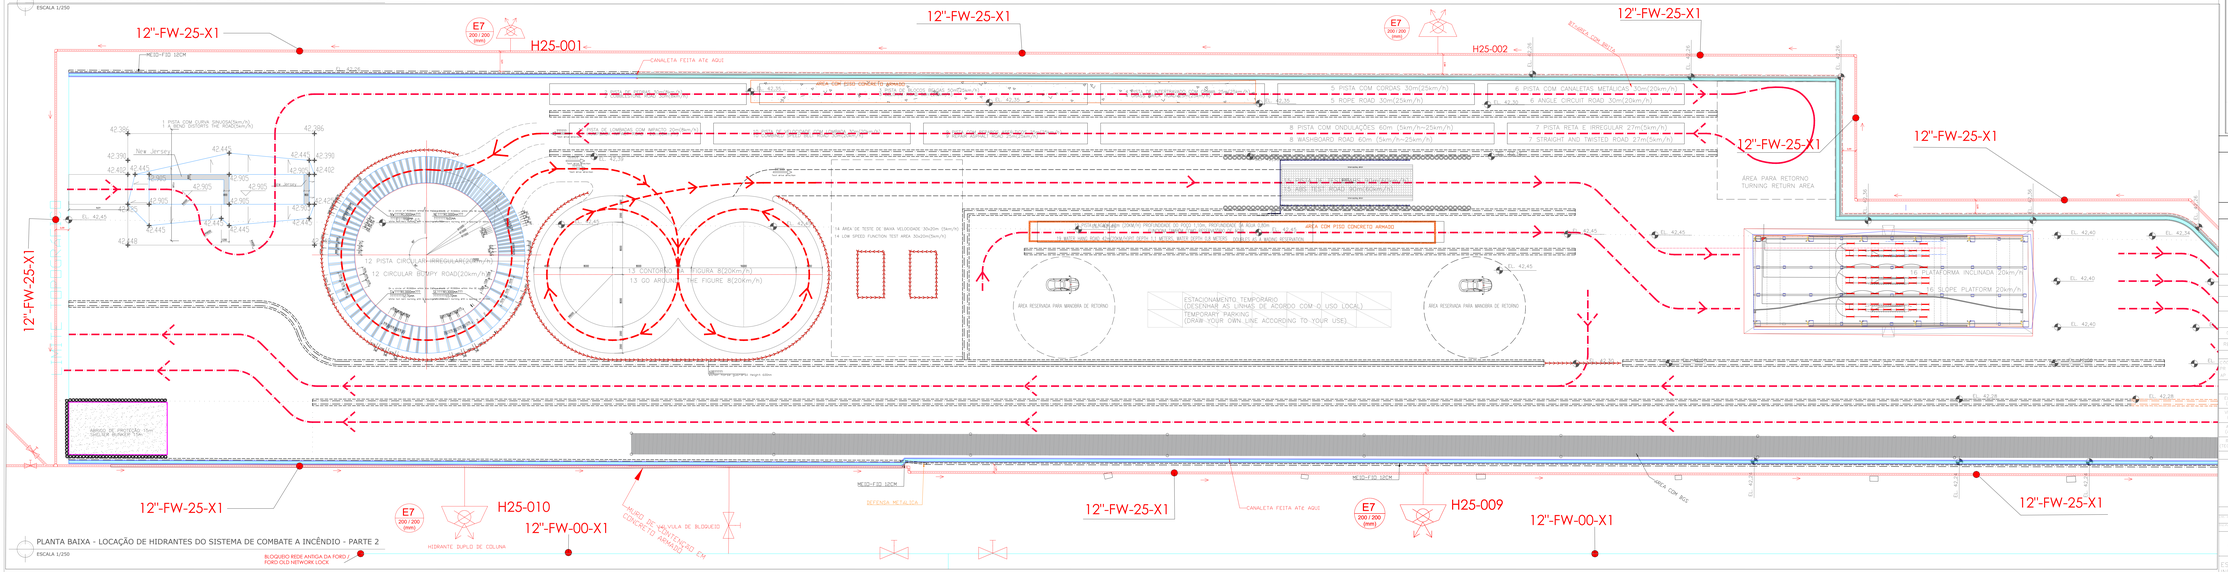

PLANTA BAIXA - LOCAÇÃO DE HIDRANTES DO SISTEMA DE COMBATE A INCÊNDIO - PARTE 2

ESCALA 1/250

NOTAS (NOTES)

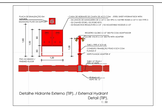

Detalhe Hidrante Externo (TIP) / External Hydrant Detail (TIP)
1 : 50

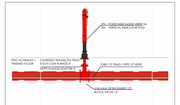

Detalhe Válvula de Bloqueio (TIP) /Block Valve Detail (TIP)
1 : 50

LEGENDA (LEGEND)

LEGENDA GERAL - SÍMBOLOS EQUIPAMENTOS / GENERAL LEGEND - EQUIPMENT SYMBOLS	
	VÁLVULA DE GOVERNO E ALARME / CHECK VALVE
	VÁLVULA DE BLOQUEIO / BLOCK VALVE
	HIDRANTE DUPLO DE COLUNA / DOUBLE COLUMN HYDRANT
	CAMIÃO MONITOR / FIRE WATER MONITOR CANNON
	BOMBAS DE INCÊNDIO / FIRE PUMPS
	RESERVA TÉCNICA DE INCÊNDIO / TECHNICAL WATER RESERVE FOR FIRE
	TUBULAÇÃO DA REDE DE INCÊNDIO / FIRE NETWORK PIPING

DOCUMENTOS DE REFERÊNCIA (REFERENCE DOCUMENTS)

PLANTA CHAVE (KEY PLANT)

REV.	DATE (DATE)	DESCRIÇÃO (DESCRIPTION)	TÉCNICO (TECHNICAL)	VERIFICAÇÃO (VERIFICATION)	APROVAÇÃO (APPROVAL)
0	14/01/2024	EMISSÃO INICIAL / ISSUE IN	RA	RC	

REVISÕES (REVIEWS)

TIPOS DE EMISSÃO (ISSUE CODES): EP - PRELIMINAR (PR - PRELIMINARY) AP - APROVAÇÃO (AP - APPROVAL)	EX - EXECUTIVO (AS-BUILT) LC - CONSTRUÇÃO (LC - CONSTRUCTION) LO - LEGAL (LO - LEGAL)	RESPONSÁVEIS (RESPONSIBLE):	
CLASSIFICADOR (DESIGNER)	CLASSIFICADOR (DESIGNER)	DATA (DATE)	CREA / CAU (CREA / CAU)
CLASSIFICADOR (DESIGNER)	BRUNNO ALMEIDA	14/01/2024	171103134-3
VERIFICADOR (VERIFIER)	RAMON CRUZ	14/01/2024	191055181-3
APROVADOR (APPROVER)			
GERENTE TÉCNICO (MANAGER)	PAULO VITOR	14/01/2024	171103134

SEPENG ENGENHARIA
AVENIDA JOÃO DIAS, 1553 - SANTO AMARO - SÃO PAULO - SP - CEP 04705-000 - BRASIL
TEL.: (11) 5687-2000 - FAX: (11) 5687-2000

BYD Motors Brasil
Avenida Henry Ford, 2000 - Polo Industrial de Camaçari

AVENIDA HENRY FORD - CAMAÇARI - BAHIA	CAMAÇARI - BAHIA - BRASIL
CNPJ: 09.405.960/0001-30	

CLIENTE / CLIENT: FIRESTARTING

PISTA DE TESTES / TEST TRACK

LOCAÇÃO DE HIDRANTES DO SISTEMA DE COMBATE A INCÊNDIO / LOCATION OF FIRE HYDRANTS IN THE FIRE FIGHTING SYSTEM

ESCALAS INDICADAS	DW-PH20.00.GE/ED.PP0-122	0	E1